
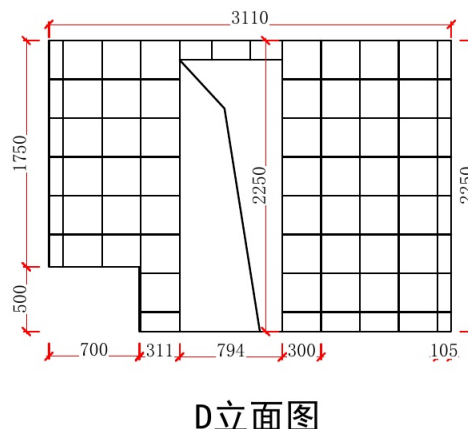
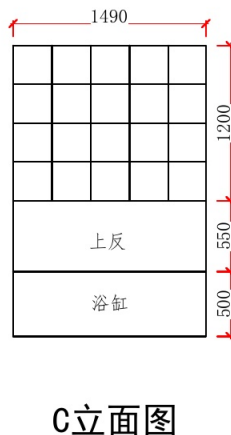
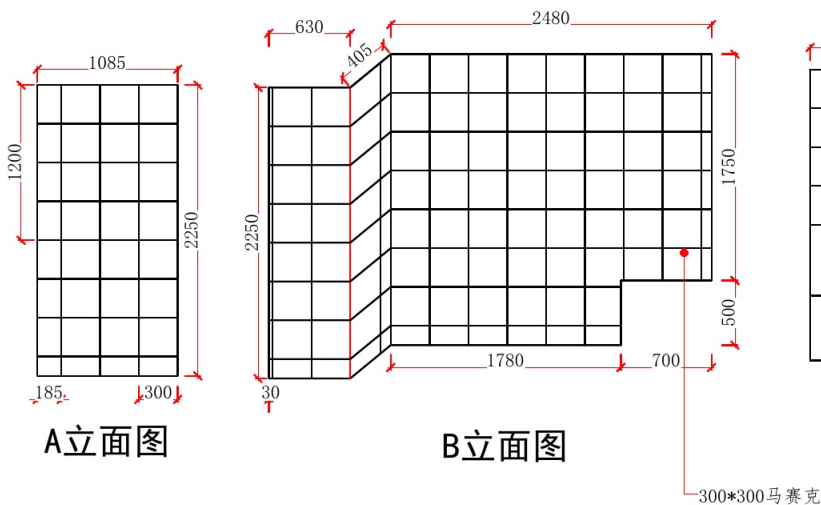


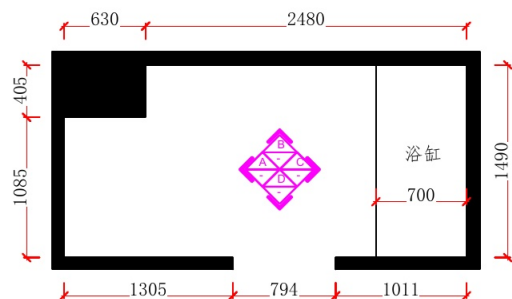

DESIGN CONTENT 设计说明

设计师对本方案拥有版权及所有权。本方案不得以任何方式修改及复制。未经设计师书面授权，本方案不得向任何第三方转让。

1、除特殊标注外，所有尺寸标注以毫米为单位。

2、平面标注为参考尺寸，需由施工方现场核实，如有差异，需及时通知设计师，并得到必要的澄清。

3、图纸设计布局原则上不做调整，如有变化，会另行说明。

4、该图纸为施工图纸，双方（客户和设计师）签字认可后，方可指导施工。

____年____月____日

OWNER SIGNATURE 业主签字

____年____月____日

DESIGNER SIGNATURE 设计师签字

____年____月____日

PROJECT 工程项目

DWG.NO 图纸编号

P-11

PAGE 页码

图纸仅供参考，以现场实际施工尺寸为准！**红色线是海棠角**

图纸空间：卫生间

墙砖规格：300*300

图例



DESIGN CONTENT
设计说明

设计师对本方案拥有版权及所有权。本方案不得以任何方式修改及复制。未经设计师书面授权，本方案不得向任何第三方转让。

1、除特殊标注外，所有尺寸标注以毫米为单位。

2、平面标注为参考尺寸，需由施工方现场核实，如有差异，需及时通知设计师，并得到必要的澄清。

3、图纸设计布局原则上不做调整，如有变化，会另行说明。

4、该图纸为施工图纸，双方（客户和设计师）签字认可后，方可指导施工。

_____年____月____日

OWNER SIGNATURE
业主签字

_____年____月____日

DESIGNER SIGNATURE
设计师签字


_____年____月____日

PROJECT
工程项目

DWG.NO
图纸编号

P-11

PAGE
页码

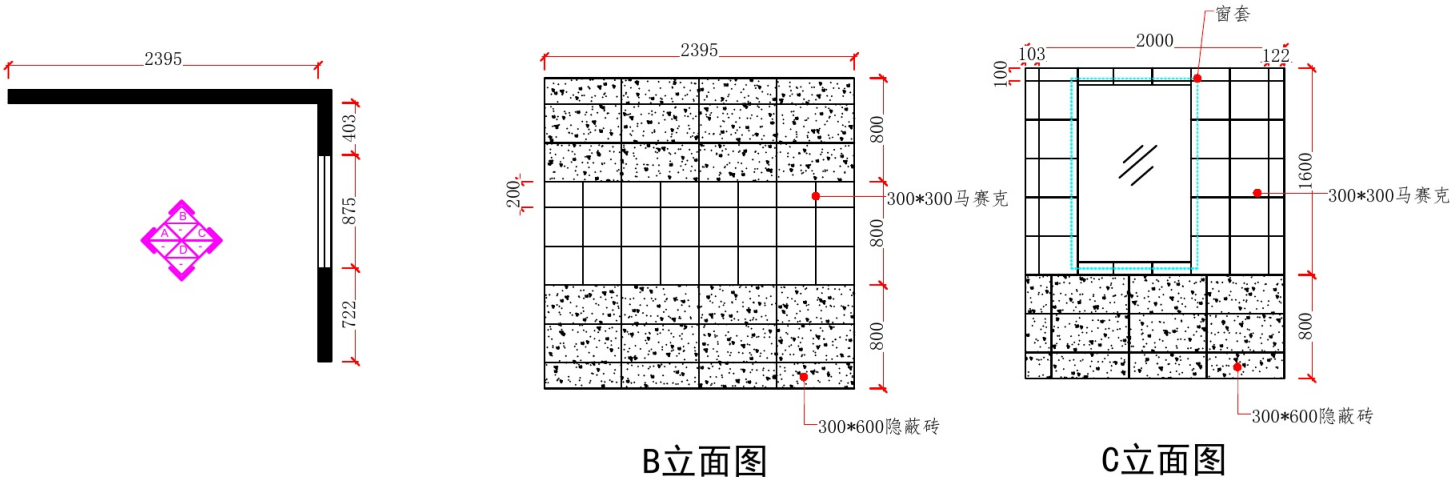

图纸仅供参考，以现场实际施工尺寸为准！红色线是海棠角

图纸空间：厨房

墙砖规格：300*300 300*600

图例

